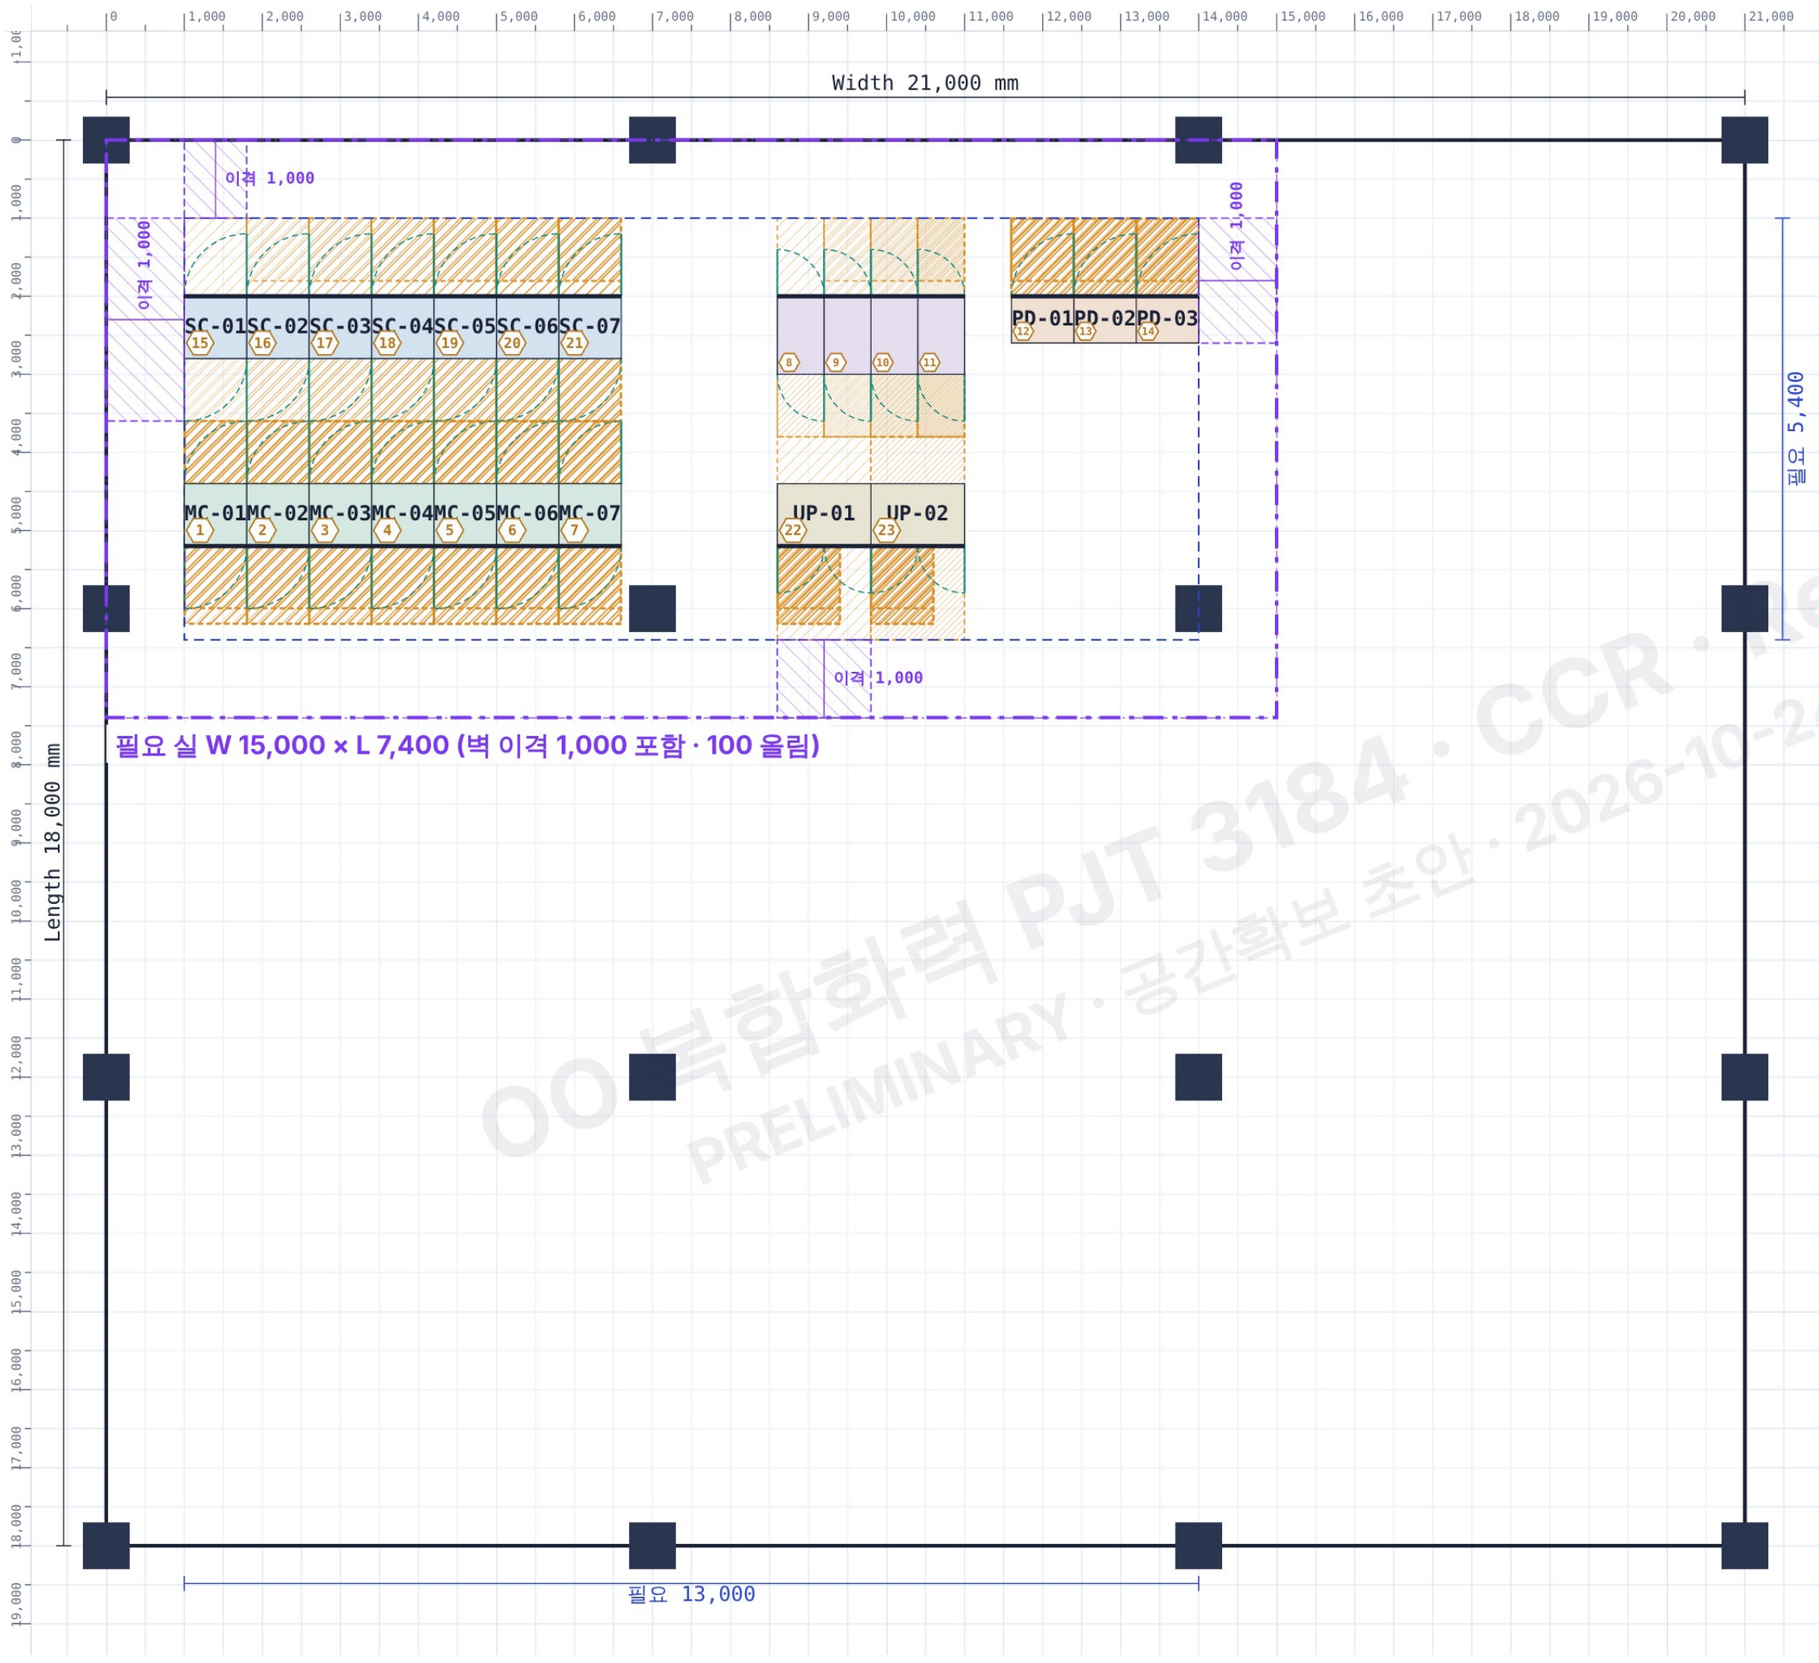


건축 전달 — 필요 사이즈

필요 실 크기 (권장 내부 치수)

W 15,000 × L 7,400

= 111.0 m² (100 단위 올림)

벽과의 이격 (사방)

1,000 mm 이상

위쪽: 지금 1,000
아래쪽: 지금 11,600
왼쪽: 지금 1,000
오른쪽: 지금 7,000

필요 영역 (판넬 + 유지보수 + 도어)

13,000 × 5,400 = 70.2 m²
Spare 0% (미적용)

검토한 실

21,000 × 18,000

판넬

System Cabinet 7 EA
Marshalling Cabinet 7 EA
Network / Server Rack 4 EA
Power Distribution 3 EA
UPS / Battery 2 EA
합계 23 EA

범례

· 굵은 선 = 판넬 전면
· 주황 빗금 = 유지보수 공간
· 파란 점선 = 필요 영역 외곽
· 보라 일점쇄선 · 띠 = 벽 이격선
· 청록 호 = 도어 회전 궤적
· 아래쪽 색 띠 = 공급 Scope

OO복합화력 PJT 3184 · CCR · Rev B · 2026-10-24
PRELIMINARY · 공간확보 초안

Rev B | 2026-10-24 출력

건축 전달 — 계장 Control Room 필요 사이즈

프로젝트 OO 복합화력 PJT 3184 · Room CCR · Rev B · 작성 홍길동 · 2026-10-24 · 단위 mm

■ 필요 실 크기 (권장 내부 치수, 100 단위 올림)

W 15,000 × L 7,400 = 111.0 m²
= 필요 영역 13,000 × 5,400 + 벽 이격 1,000 × 양쪽

■ 벽과의 이격 (판넬 · 유지보수 공간 외곽 → 벽)

위 · 아래 · 왼쪽 · 오른쪽 모두 1,000 mm 이상
지금 검토한 실(21,000 × 18,000) 기준 실제: 위쪽 1,000 / 아래쪽 11,600 / 왼쪽 1,000 / 오른쪽 7,000

■ 산정 조건

1) 필요 영역 = 판넬 몸체 + 전면 · 후면 유지보수 공간 + 도어 회전 궤적의 외곽 (13,000 × 5,400 = 70.2 m²)
2) Spare: Spare 0% (미적용)
3) 벽 이격: 1,000 mm (사방)
4) 판넬 간 최소 이격 0 mm (줄로 맞닿은 판넬은 예외) · 도어 간 최소 이격 0 mm
5) 유지보수 공간 · 도어 (Type 별)
   - System Cabinet 7 EA: 800W × 800D × 2100H, 전면 1,000 / 후면 800, 도어 전·후면 L 힌지 (회전 반경 800)
   - Marshalling Cabinet 7 EA: 800W × 800D × 2100H, 전면 1,000 / 후면 800, 도어 전·후면 L 힌지 (회전 반경 800)
   - Network / Server Rack 4 EA: 600W × 1000D × 2100H, 전면 1,000 / 후면 800, 도어 전·후면 R 힌지 (회전 반경 600)
   - Power Distribution 3 EA: 800W × 600D × 2100H, 전면 1,000 / 후면 0, 도어 전면 L 힌지 (회전 반경 800)
   - UPS / Battery 2 EA: 1200W × 800D × 2000H, 전면 1,200 / 후면 600, 도어 전면 양개 L-R (회전 반경 600)
6) 기둥: 600 × 600, Span X 7000,7000,7000 / Y 6000,6000,6000 — 판넬 · 유지보수 공간과 겹치지 않게 배치
7) 판넬 최고 높이 2,100 — 천장 · 보 하단 높이, 상부 케이블 인입 여유는 건축 · 전기와 협의
8) 수량: 합계 23 EA, 판넬 바닥면적 14.7 m² · 공급 Scope (미지정) 23

■ 배치 검토: 간섭 0건 · 경고 0건 (위반 없음)

■ 요청 사항

- 위 필요 실 크기 · 벽 이격 기준으로 Room 초안 도면(CAD) 회신
- 출입문 위치, 케이블 인입(Floor / Trench) 위치, Access Floor 여부 · 높이 확인
- 본 수치는 초기 공간확보용 — 상세 판넬 배치는 건축 CAD 수령 후 계장에서 확정

■ Equipment List

1	MC-01	Marshalling Cabinet	800×800×2100
2	MC-02	Marshalling Cabinet	800×800×2100
3	MC-03	Marshalling Cabinet	800×800×2100
4	MC-04	Marshalling Cabinet	800×800×2100
5	MC-05	Marshalling Cabinet	800×800×2100
6	MC-06	Marshalling Cabinet	800×800×2100
7	MC-07	Marshalling Cabinet	800×800×2100
8	NR-01	Network / Server Rack	600×1000×2100
9	NR-02	Network / Server Rack	600×1000×2100
10	NR-03	Network / Server Rack	600×1000×2100
11	NR-04	Network / Server Rack	600×1000×2100
12	PD-01	Power Distribution	800×600×2100
13	PD-02	Power Distribution	800×600×2100
14	PD-03	Power Distribution	800×600×2100
15	SC-01	System Cabinet	800×800×2100
16	SC-02	System Cabinet	800×800×2100
17	SC-03	System Cabinet	800×800×2100
18	SC-04	System Cabinet	800×800×2100
19	SC-05	System Cabinet	800×800×2100
20	SC-06	System Cabinet	800×800×2100
21	SC-07	System Cabinet	800×800×2100
22	UP-01	UPS / Battery	1200×800×2000
23	UP-02	UPS / Battery	1200×800×2000

OO 복합화력 PJT 3184 · CCR · Rev B
PRELIMINARY · 공간확보 초안 · 2026-10-24